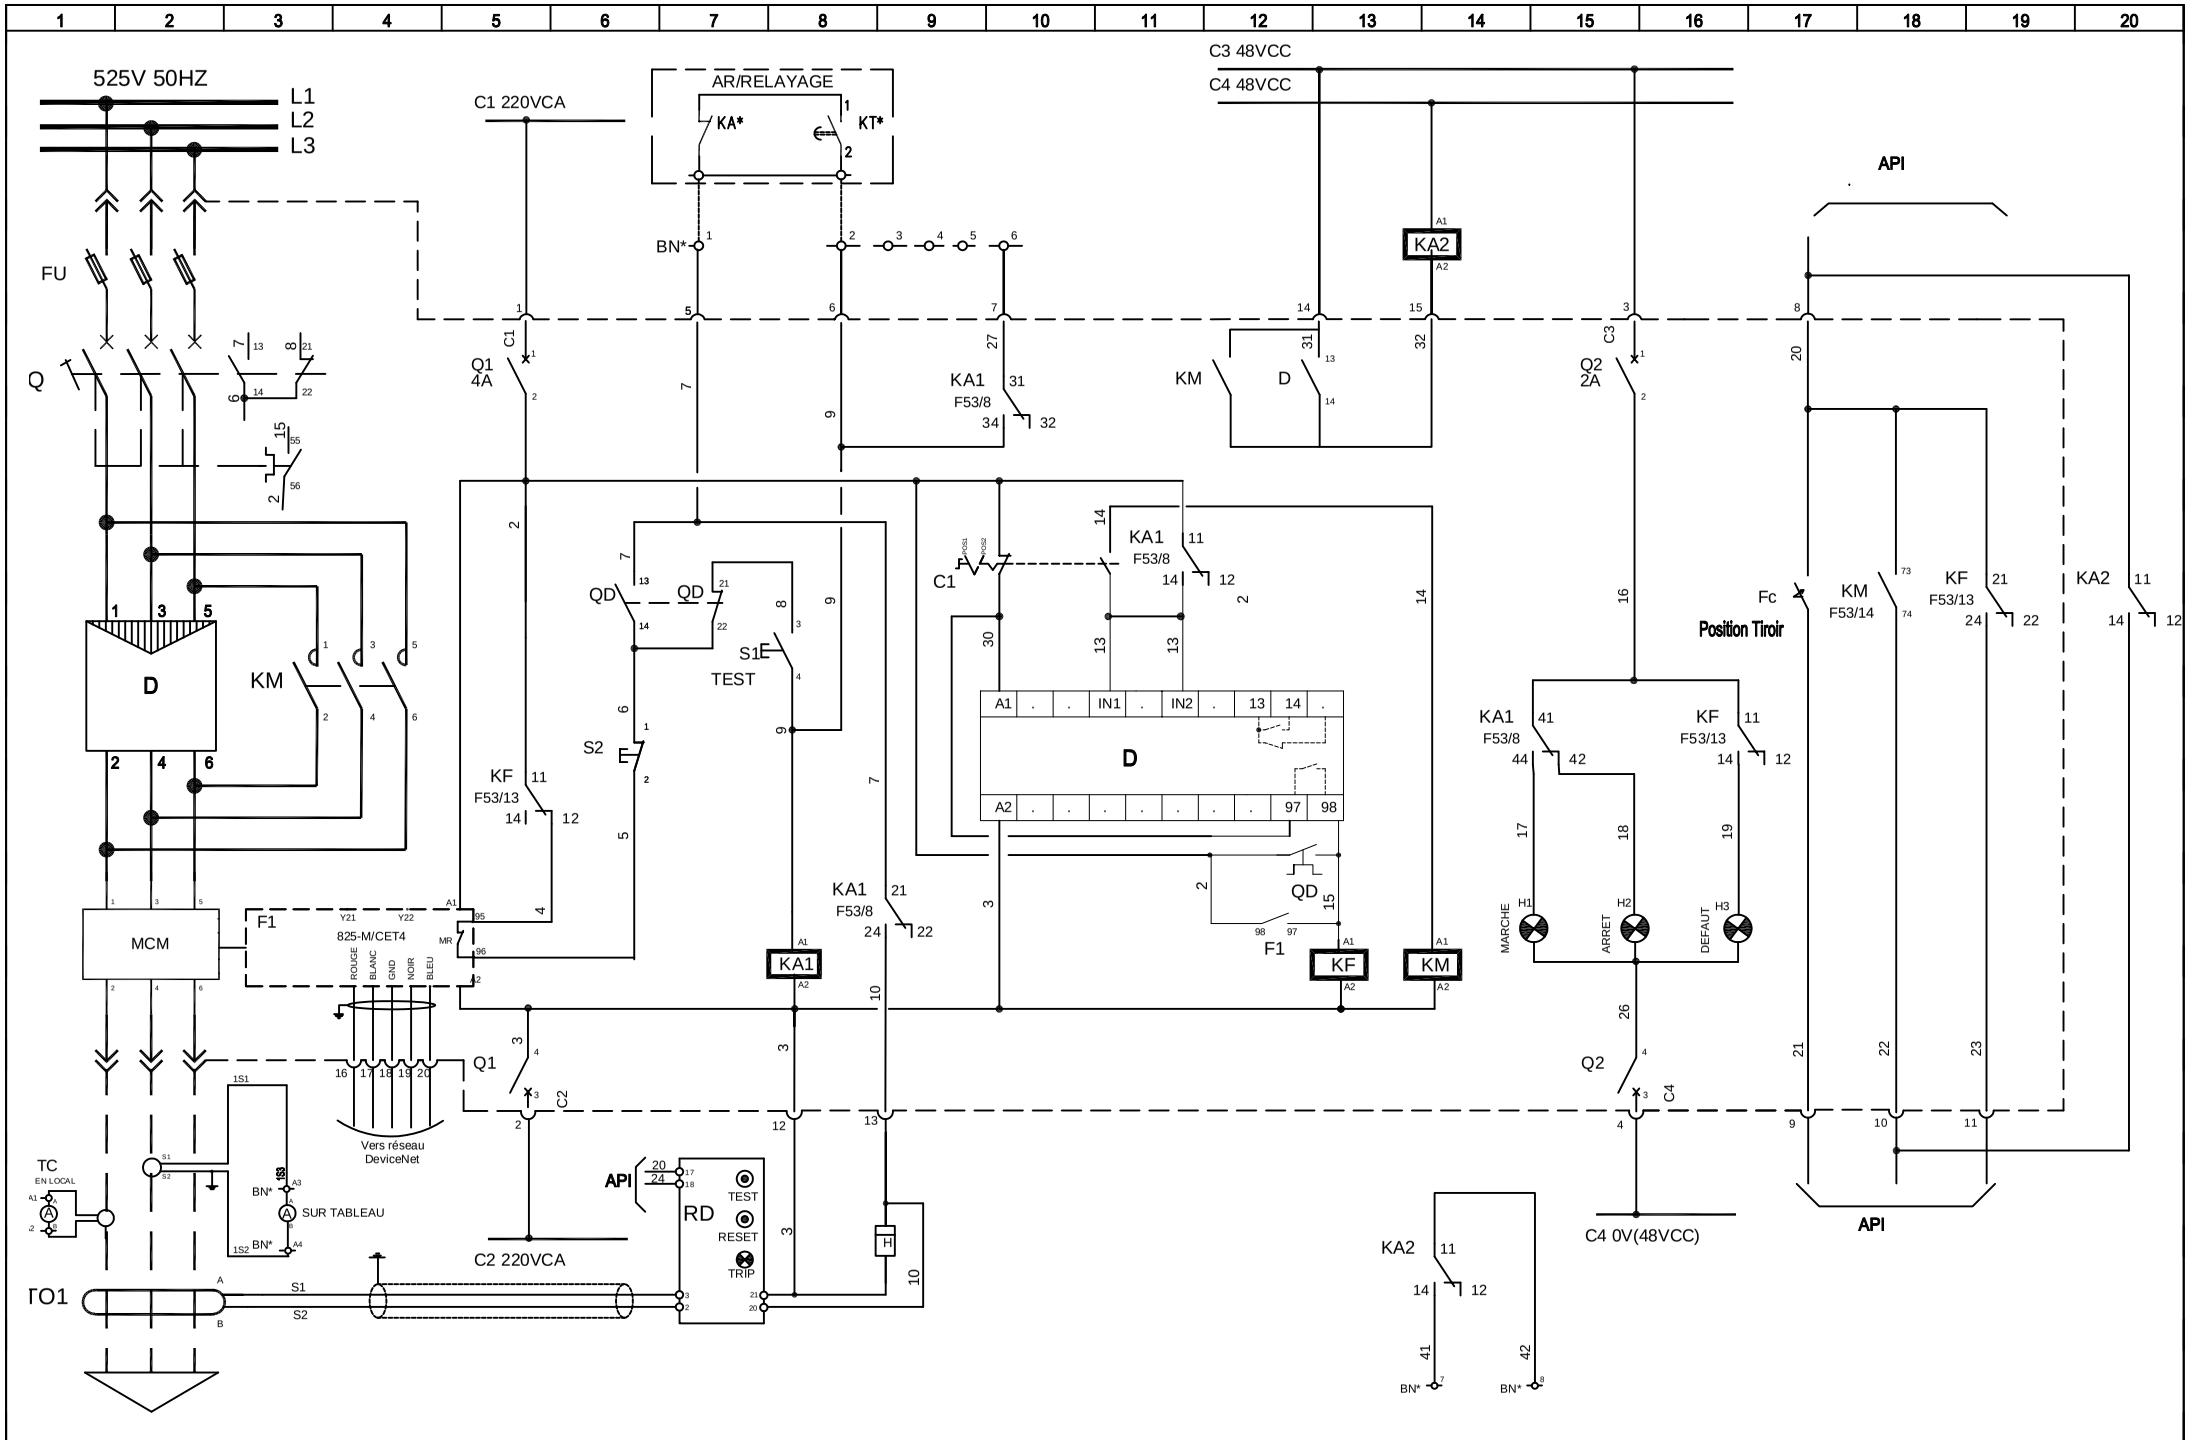

CENTRELEC Solutions Industrielles	DESSINE : W.ETTYRE	E	08-09-2006	FIN DE CHANTIER	S.MA	OCP YOUSSOUFIA
	VERIFIE : M.BO	D	14-01-2005	Mise à jour	S.MA	
		B	10-11-2004	Mise à jour	W.ET	
	DATE DE CREATION :	A	21-09-2004	Création de document	W.ET	Document n° : 120403 WE 00F

LAVERIE GANTOUR - YOUSSOUFIA -

DOSSIER DES SCHEMAS TYPES

SCHEMA TYPE A1/A (Ampermetre en local)

FOLIO 3

◁ 2 4 ▷