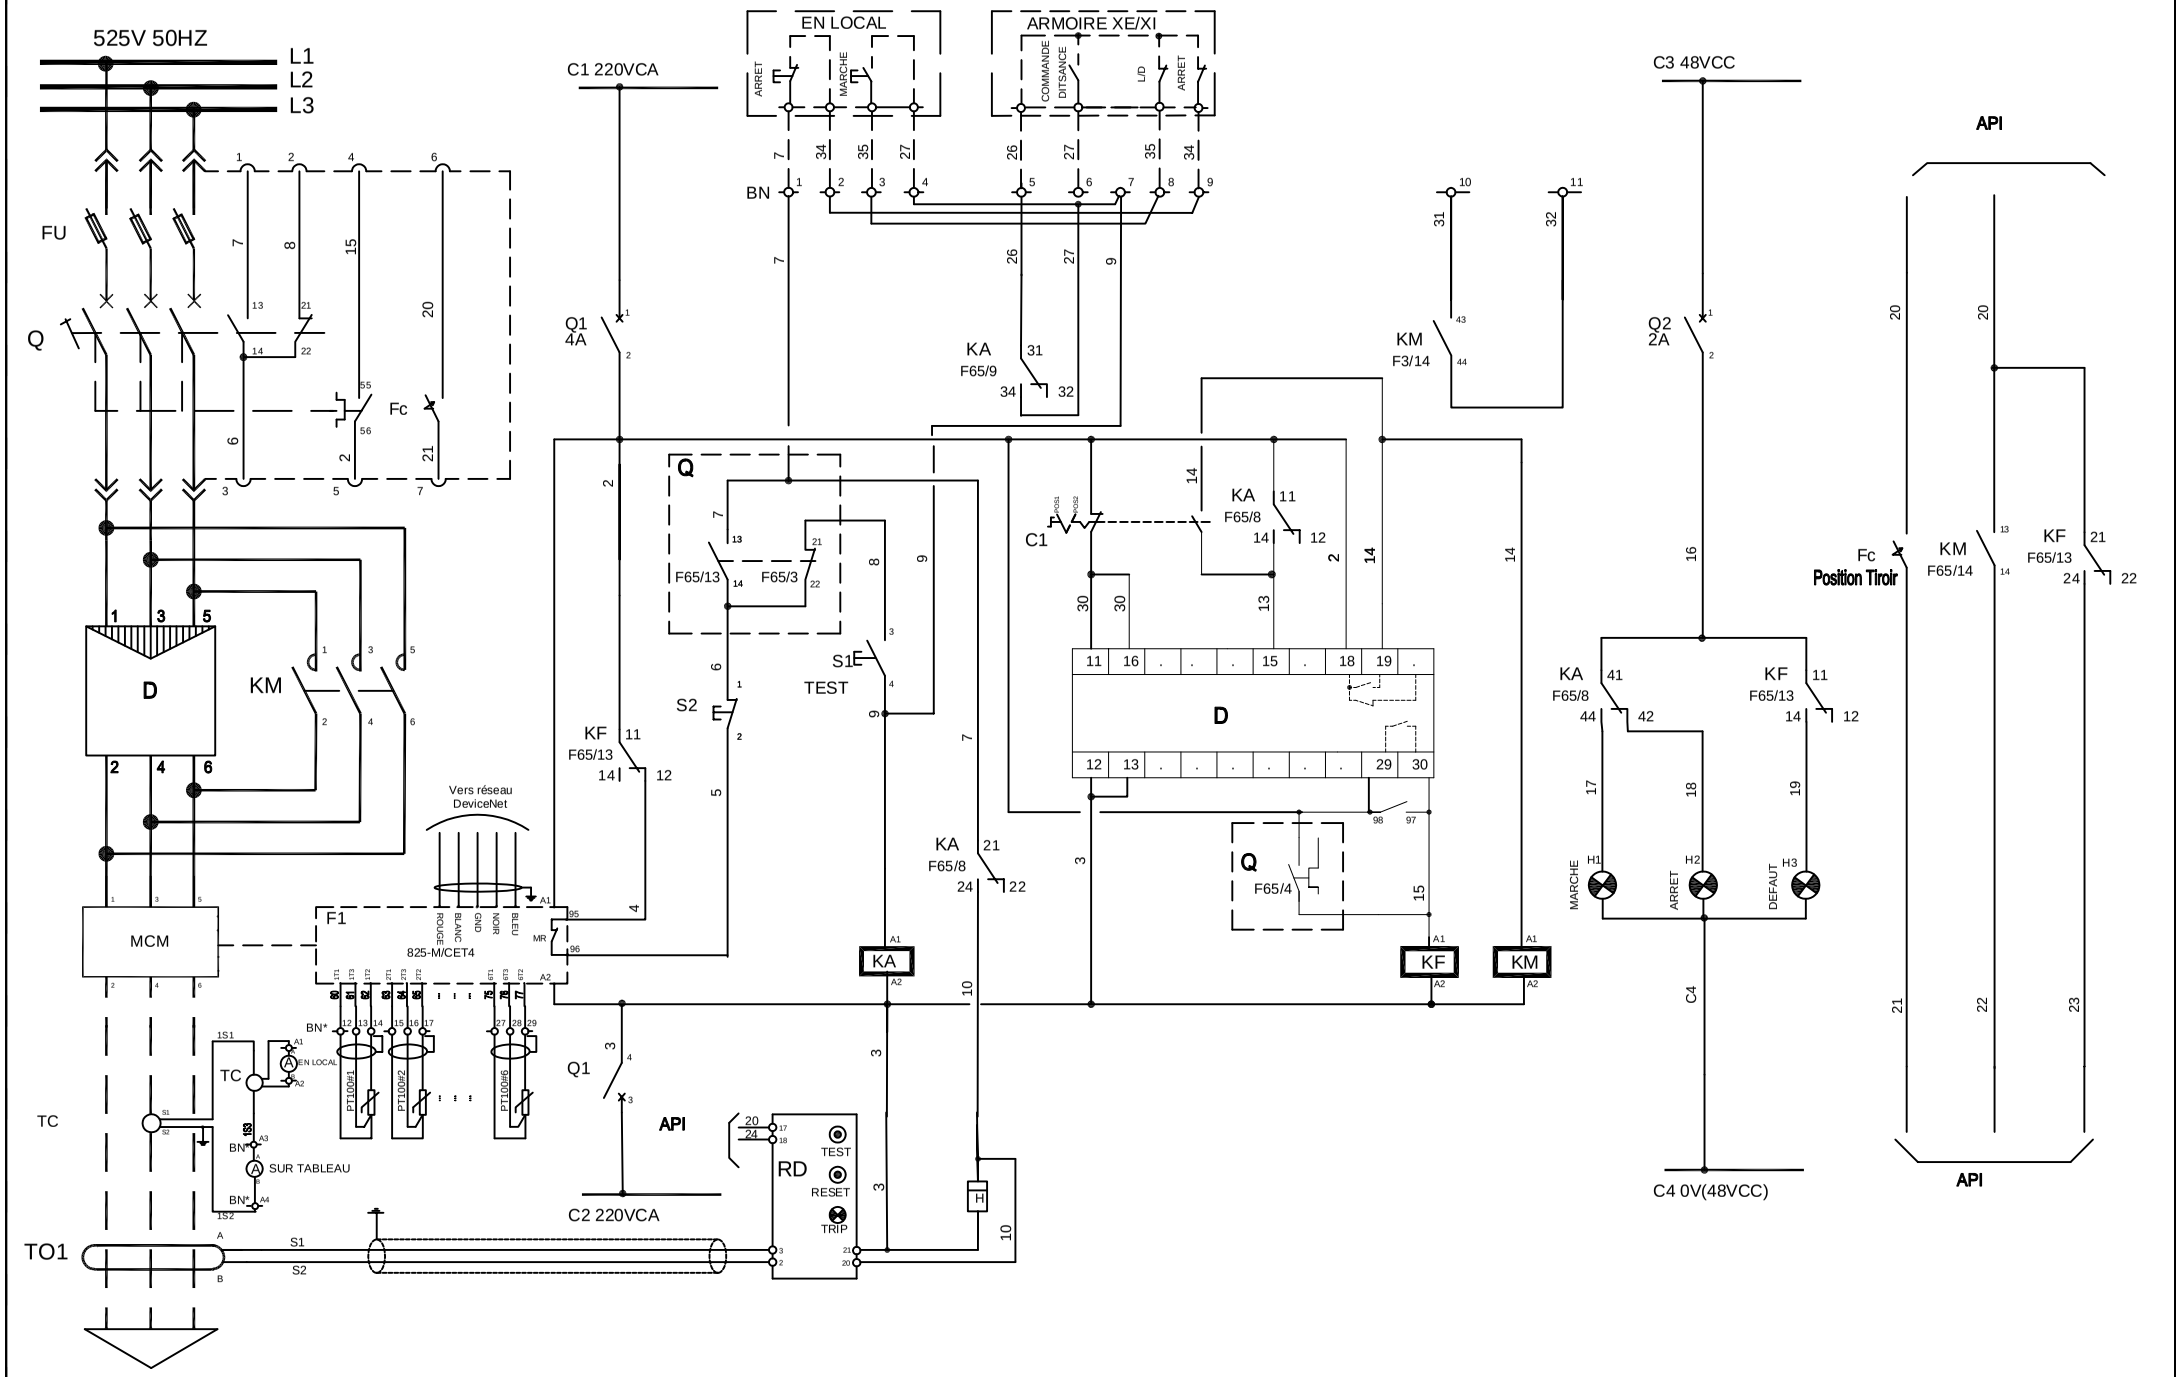


| | | | | | |
|---|---|---|---|---|---|
| CENTRELEC Solutions Industrielles | DESSINE : W.ETTYRE | | | | |
| | VERIFIE : M.BO | D | 14-01-2005 | Mise à jour | S.MA |
| | DATE DE CREATION : 18/09/04 | A | 21-09-2004 | Création de document | W.ET |
| | | INDICE | DATE | MODIFICATION | DES. |

OCP YOUSSOUFIA

Document n° : **120402-WE-09F**

LAVERIE GANTOUR - YOUSSOUFIA -

DOSSIER DES SCHEMAS TYPES

SCHEMA TYPE C3/A (Ampermetre en local)

FOLIO 17

◁ 16 18 ▷

Logiciel SEE v. 2