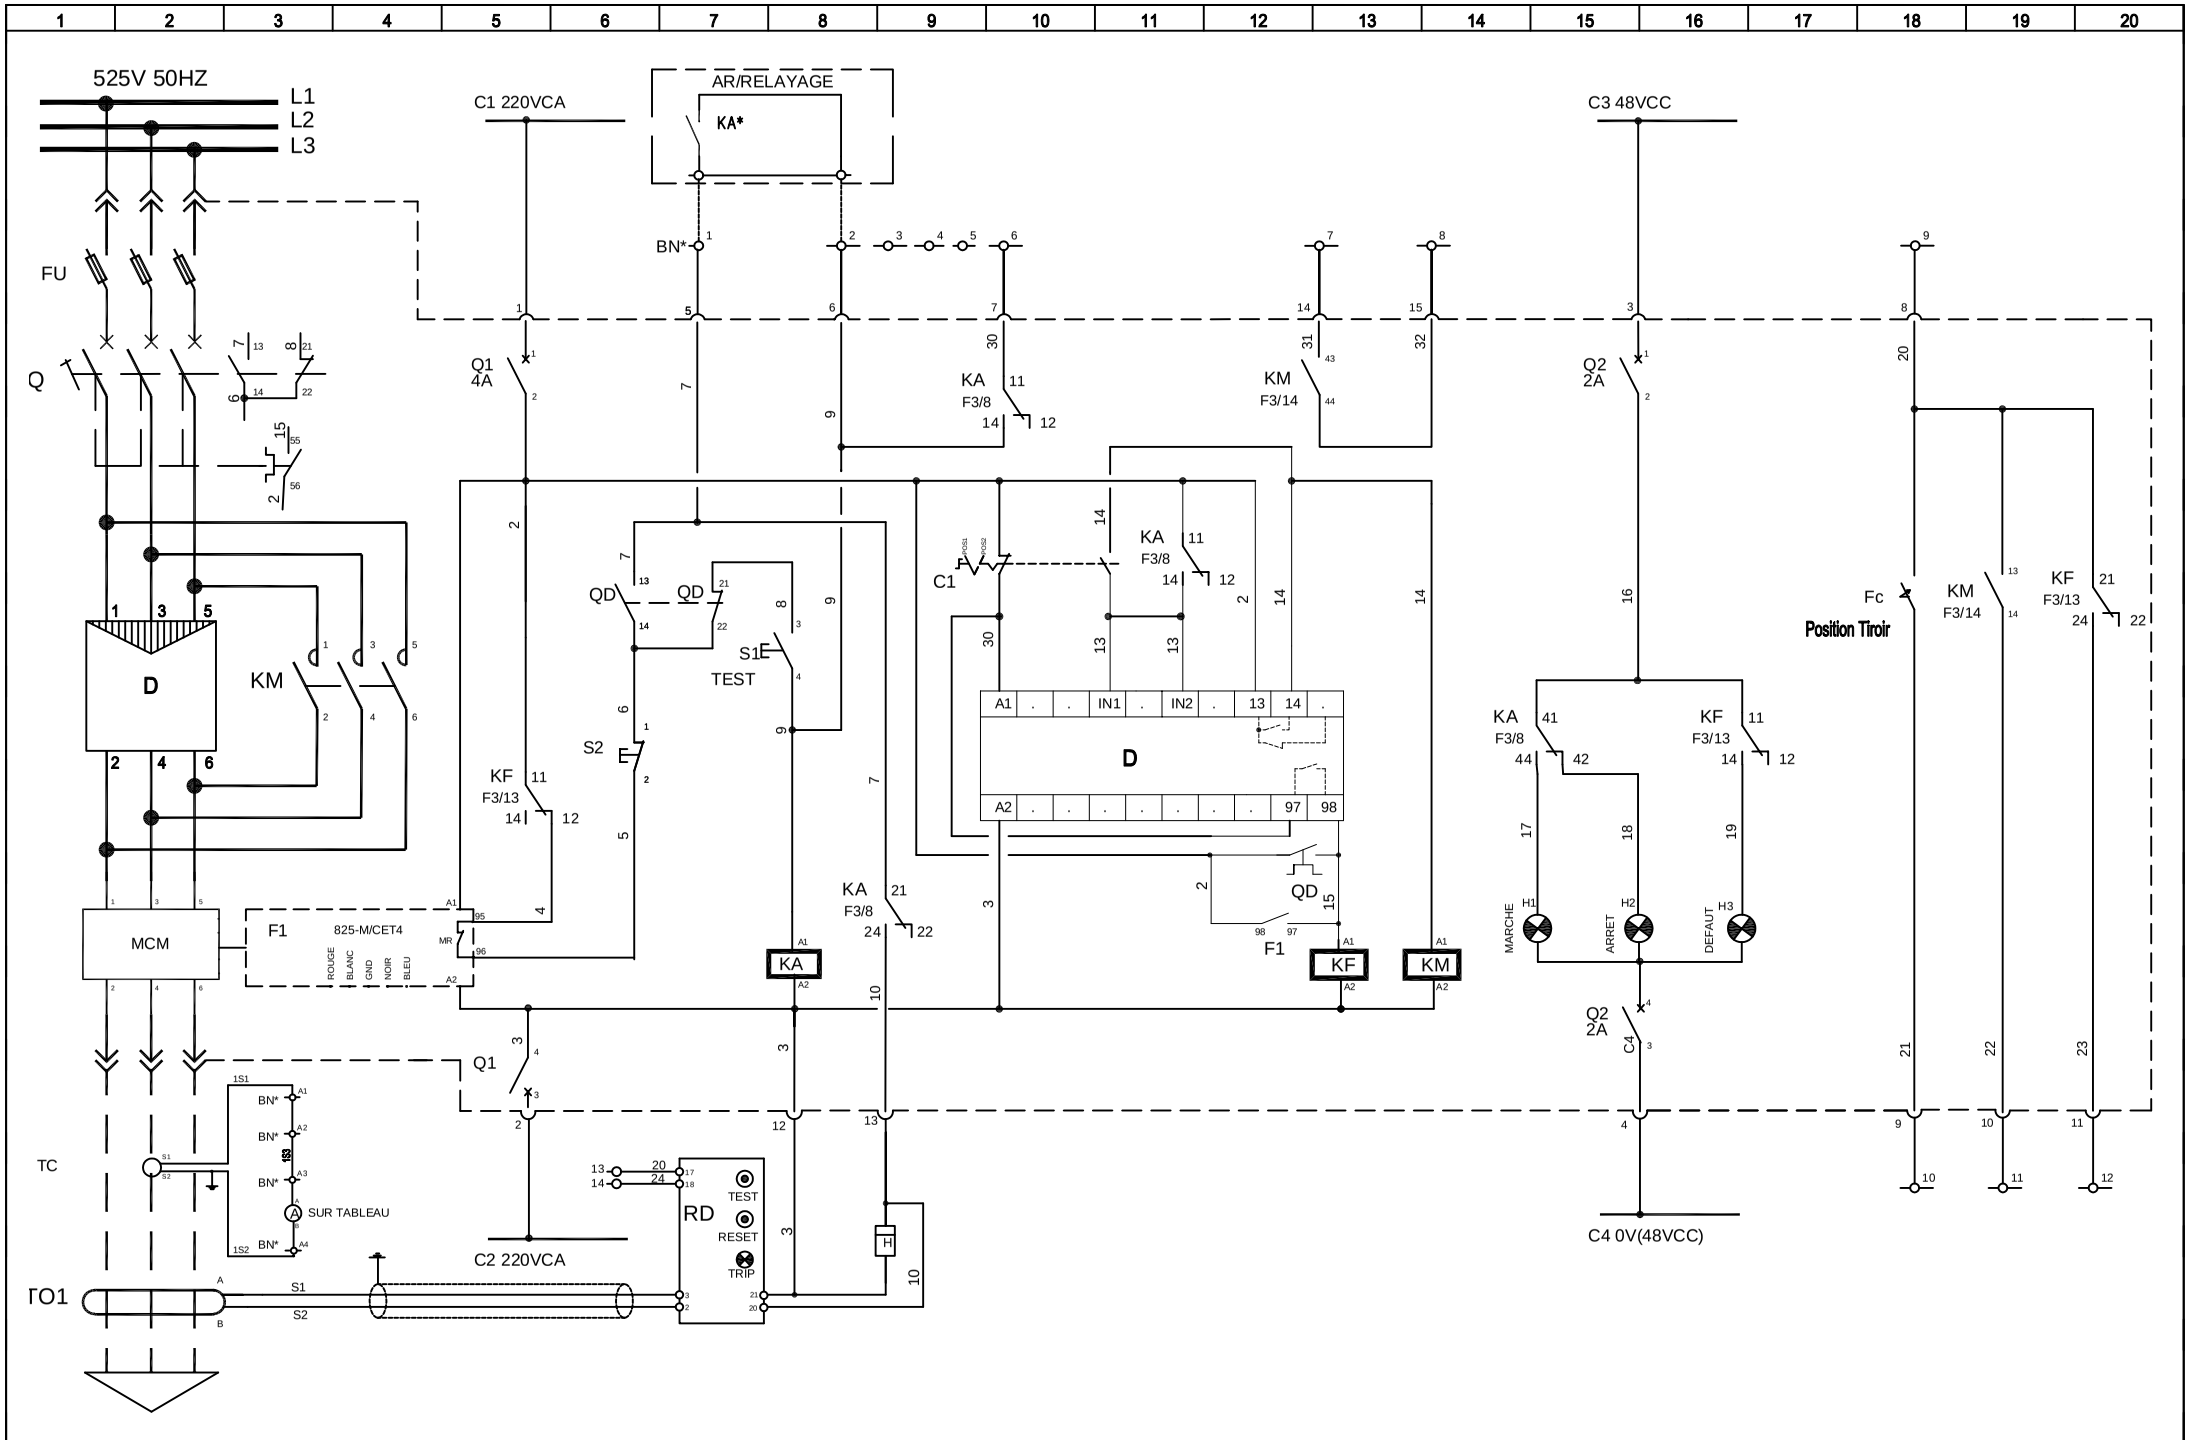

CENTRELEC Solutions Industrielles	DESSINE : W.ETTYRE	E	06-09-2006	FIN DE CHANTIER	S.MA	OCP YOUSSOUFIA
	VERIFIE : M.BO	D	14-01-2005	Mise à jour	S.MA	
		B	10-11-2004	Mise à jour	W.ET	
	DATE DE CREATION :	A	21-09-2004	Création de document	W.ET	Document n° : 130403 WE 005

LAVERIE GANTOUR - YOUSSOUFIA -
DOSSIER DES SCHEMAS TYPES
SCHEMA TYPE A4

FOLIO 9
◁ 8 10 ▷