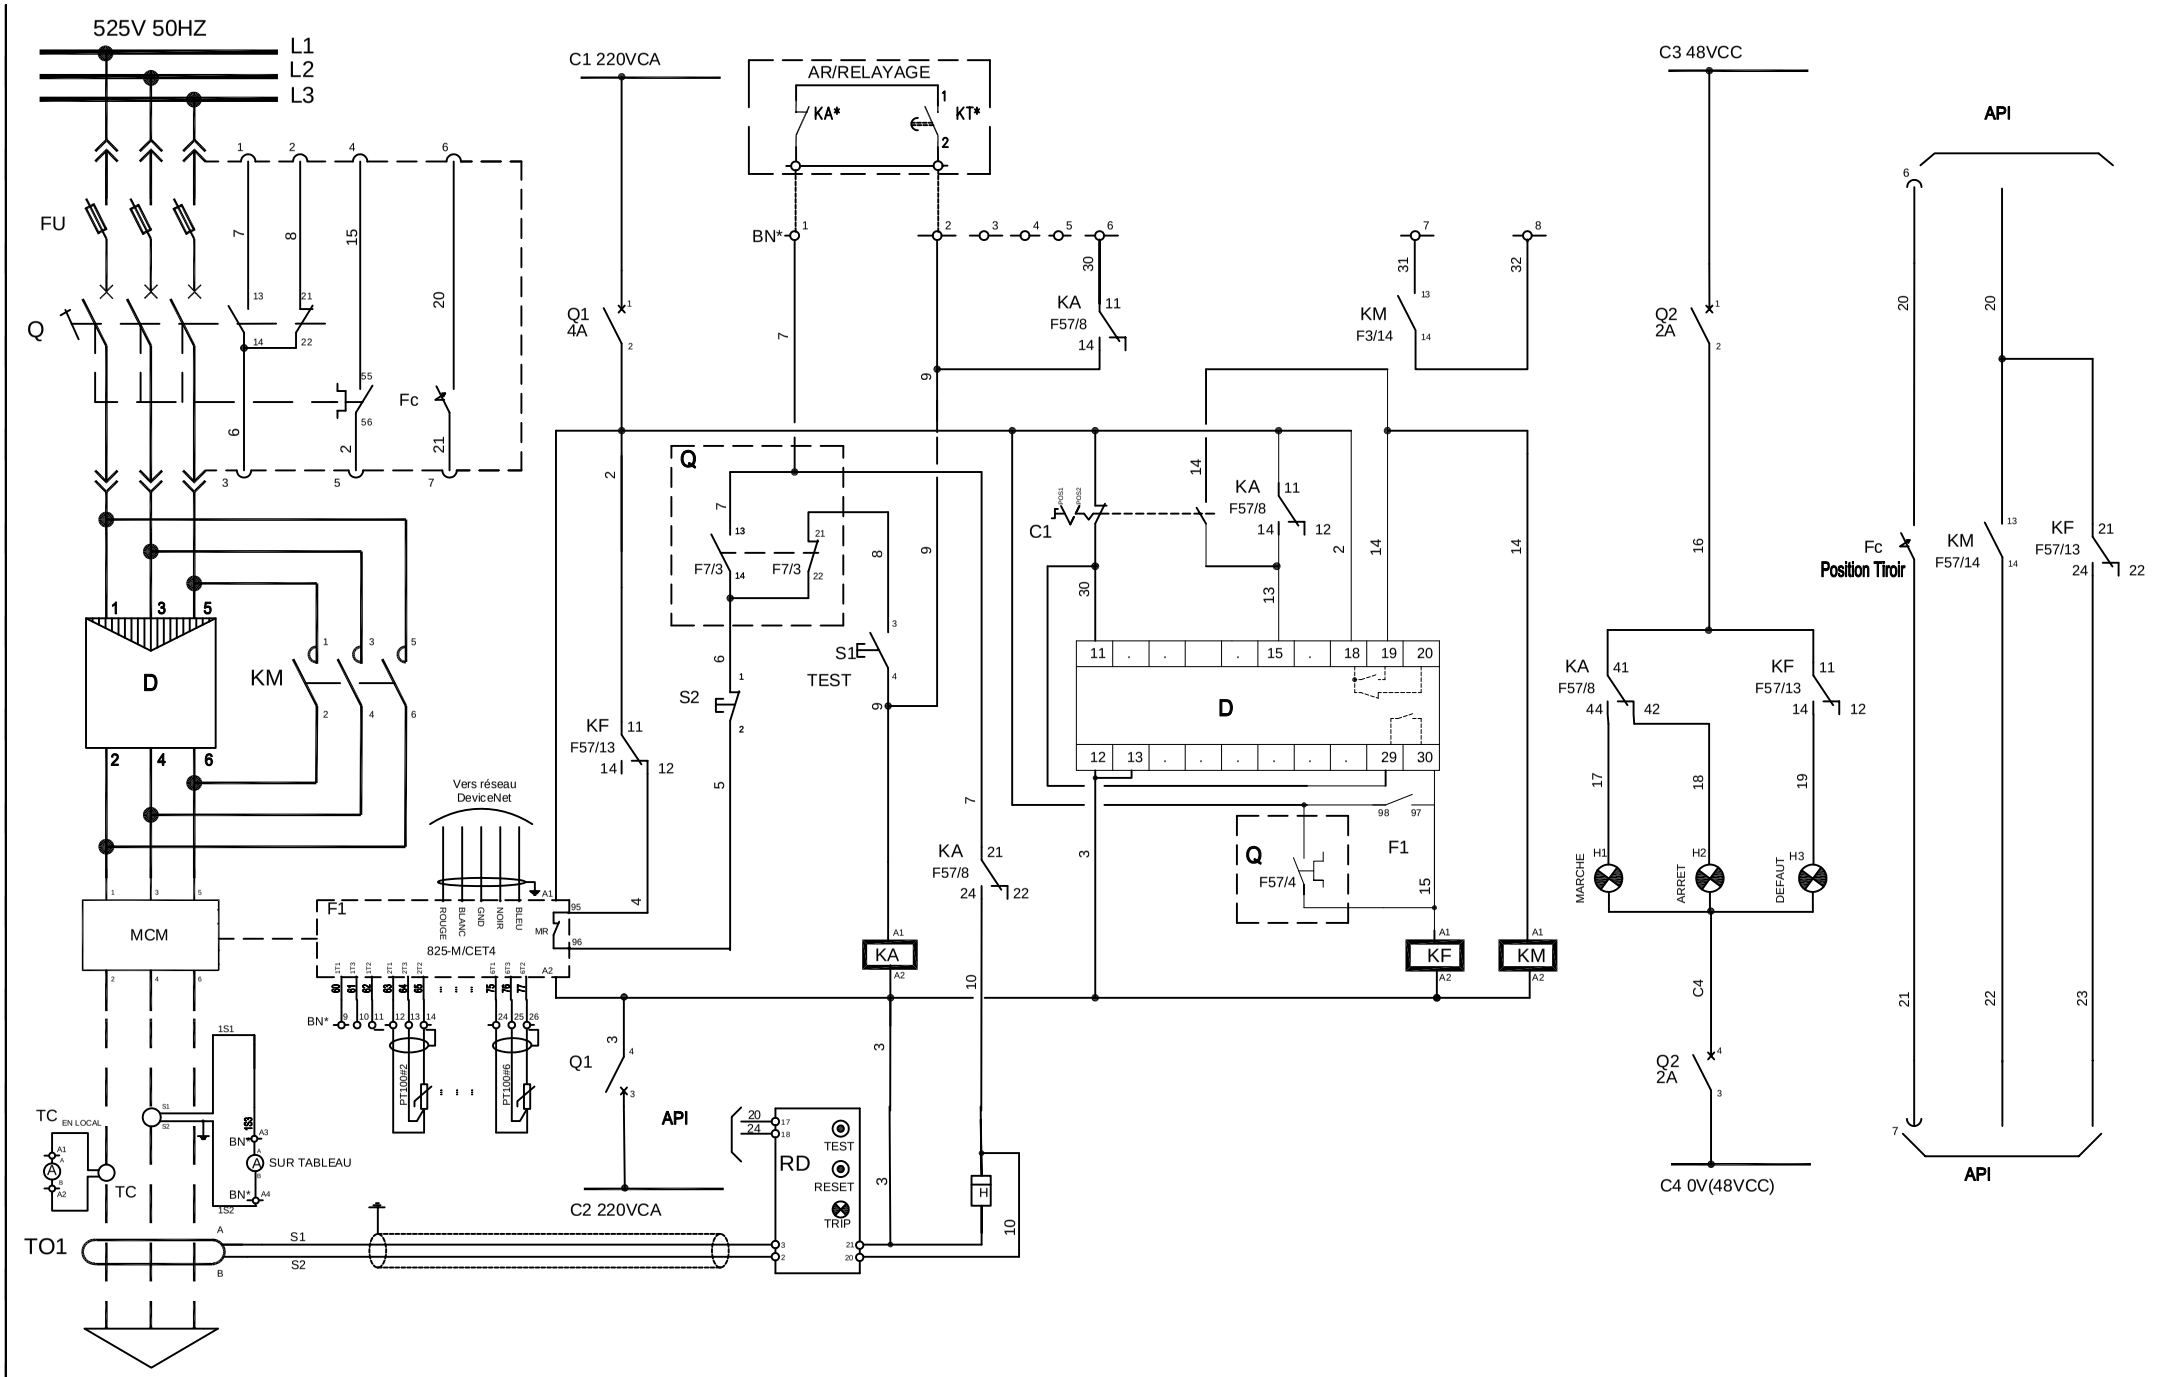

CENTRELEC Solutions Industrielles	DESSINE : W.ETTYRE	E	08-09-2006	FIN DE CHANTIER	S.MA	OCP YOUSSOUFIA	LAVERIE GANTOUR - YOUSSOUFIA -
	VERIFIE : M.BO	D	14-01-2005	Mise à jour	S.MA		DOSSIER DES SCHEMAS TYPES
		B	10-11-2004	Mise à jour	W.ET		SCHEMA TYPE A3/A (Ampermetre en local)
	DATE DE CREATION : 18/09/04	A	21-09-2004	Création de document	W.ET	Document n° : 120402-WE-09F	
		INDICE	DATE	MODIFICATION	DES.		

FOLIO 7

◁ 6 8

Logiciel SEE v.