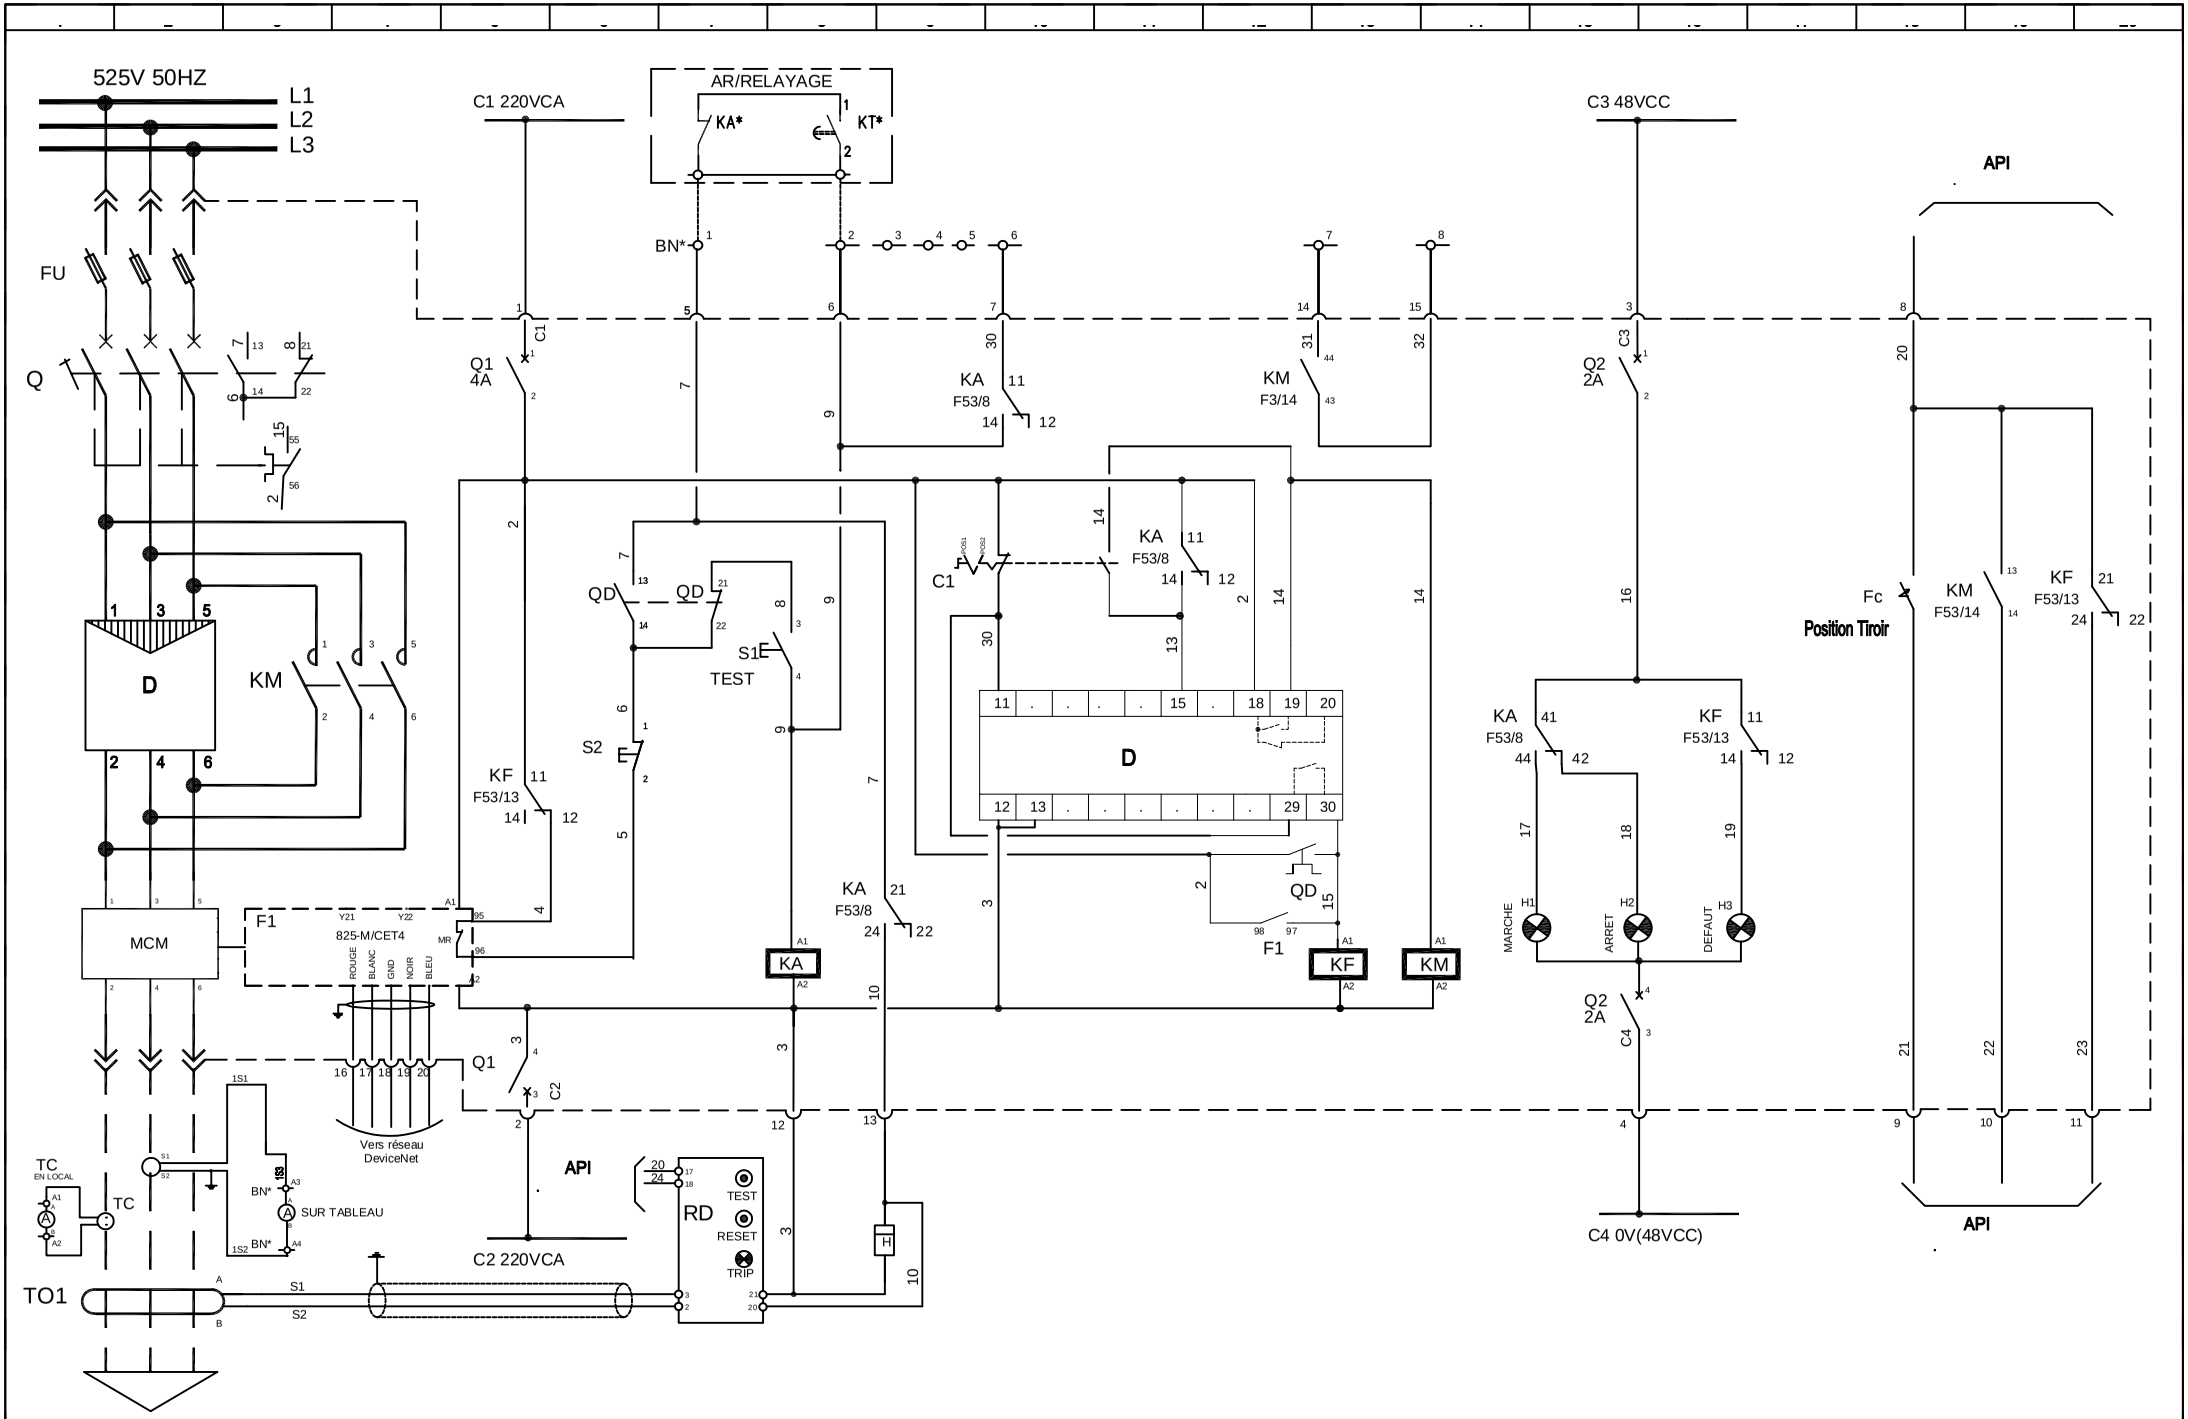

CENTRELEC Solutions Industrielles	DESSINE : W.ETTYRE	E	08-09-2006	FIN DE CHANTIER	S.MA	OCP YOUSSOUFIA
	VERIFIE : M.BO	D	14-01-2005	Mise à jour	S.MA	
		B	10-11-2004	Mise à jour	W.ET	
	DATE DE CREATION : 18/09/04	A	21-09-2004	Création de document	W.ET	Document n° : 120402-WE-09F
		INDICE	DATE	MODIFICATION	DES.	

LAVERIE GANTOUR - YOUSSOUFIA -
DOSSIER DES SCHEMAS TYPES
SCHEMA TYPE A2/A (Ampermetre en local)

FOLIO 5
◁ 4 6 ▷
Logiciel SEE v. 2